


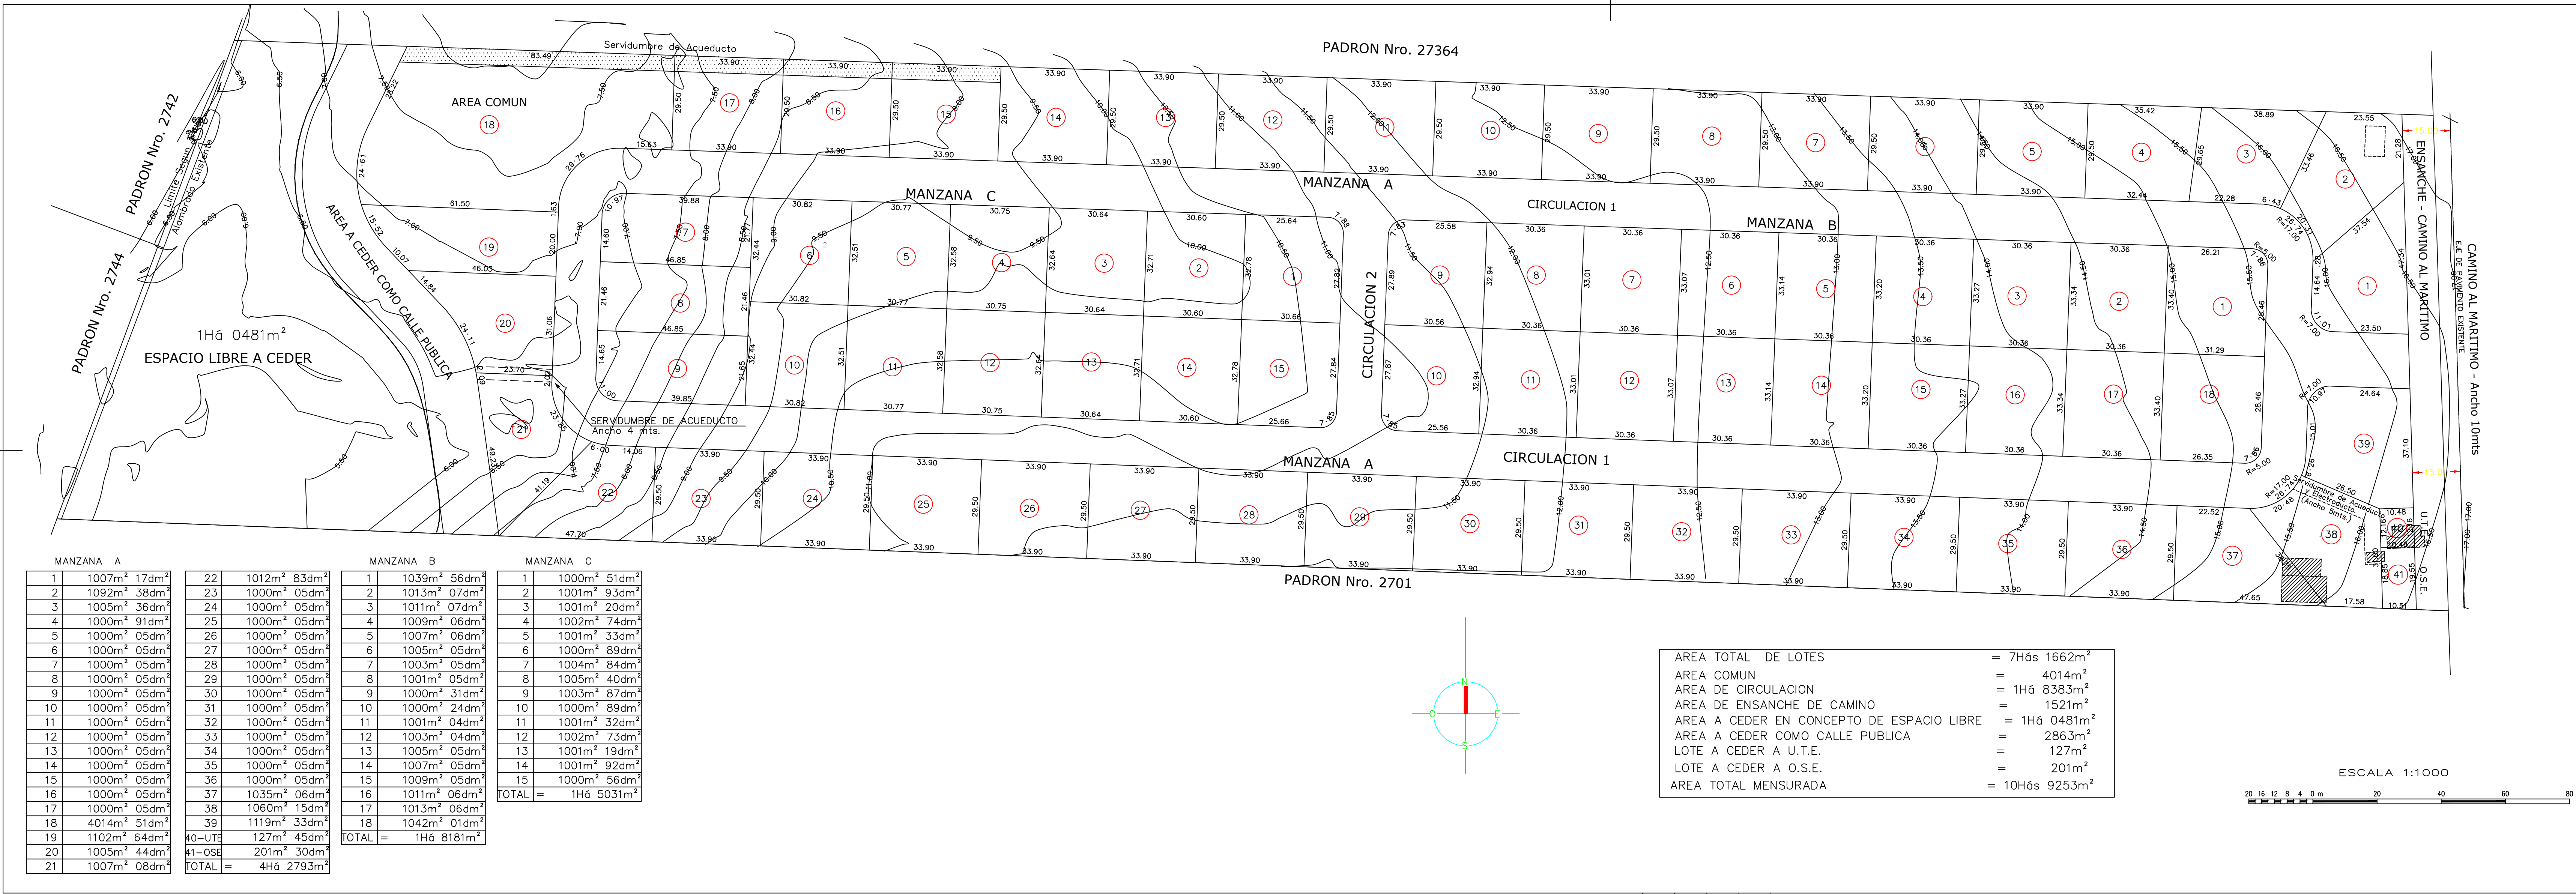

PROYECTO DE FRACCIONAMIENTO

Escala 1:1000
MAYO 2024

PADRON

2699

AREA

Has

m²

dm³

10

9253

00

Carpeta Catastral

106

Manzana Catastral

1567

Localidad Catastral

Maldonado

Departamento

Maldonado

PROPIETARIO :

CARLOS RODRIGUEZ QUEIROLO

INGENIERO AGRIMENSOR

MAT. 779

GONZALO PERDOMO GUADALUPE

INGENIERO AGRIMENSOR

MAT. 1722

ANTECEDENTES

GRAFICO Plano de Mensura y del Ing. Agrimensor Omar Hernandez de Diciembre de 1991, registrado en la Oficina Nacional de catastro el 12 de Diciembre de 1991 con el Nro. 2974.-

DOMINIALES

SOLANAS

RINCON DEL DIARIO

LAGUNA DEL DIARIO

PUNTA BALLENA